



WC SERVIÇO

ANTES


MÓVEL LAVATÓRIO

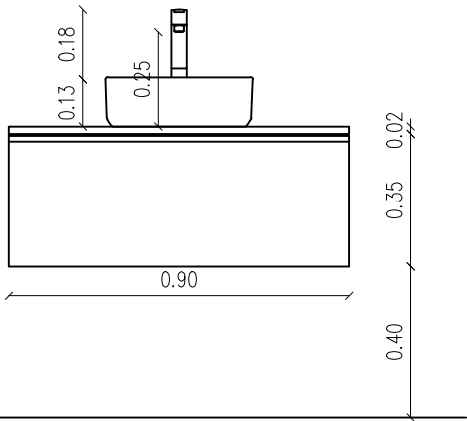

ALÇADO
ESCALA 1:20

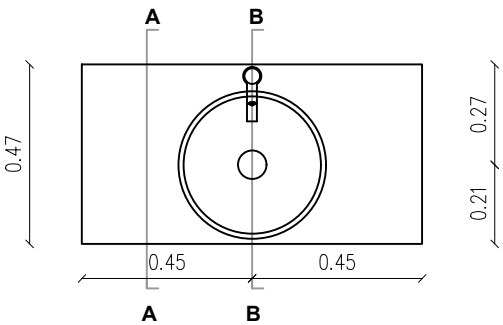


PLANTA
ESCALA 1:20

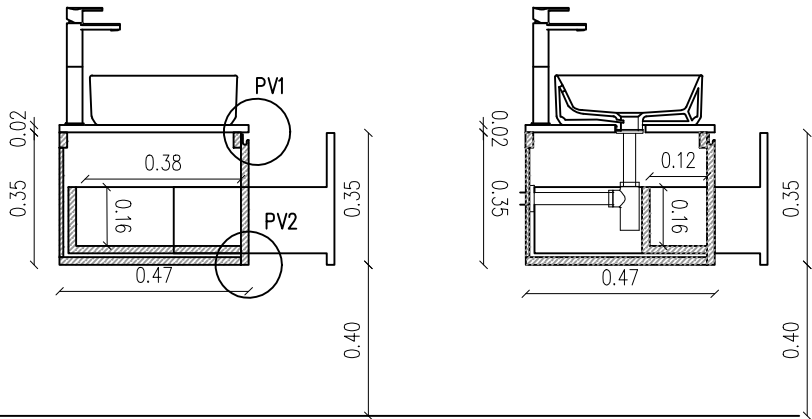


CORTE AA
ESCALA 1:20

CORTE BB
ESCALA 1:20

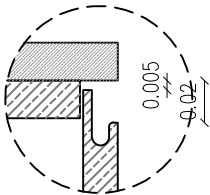


PV1
ESCALA 1:5

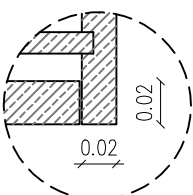


PV2
ESCALA 1:5

ATUAL


MÓVEL LAVATÓRIO

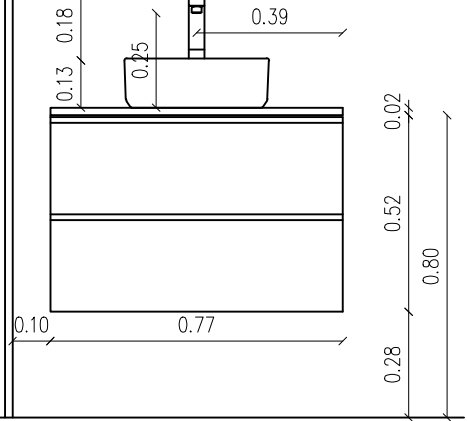

ALÇADO
ESCALA 1:20

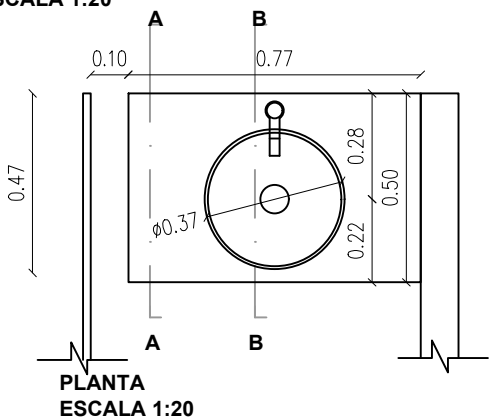


PLANTA
ESCALA 1:20

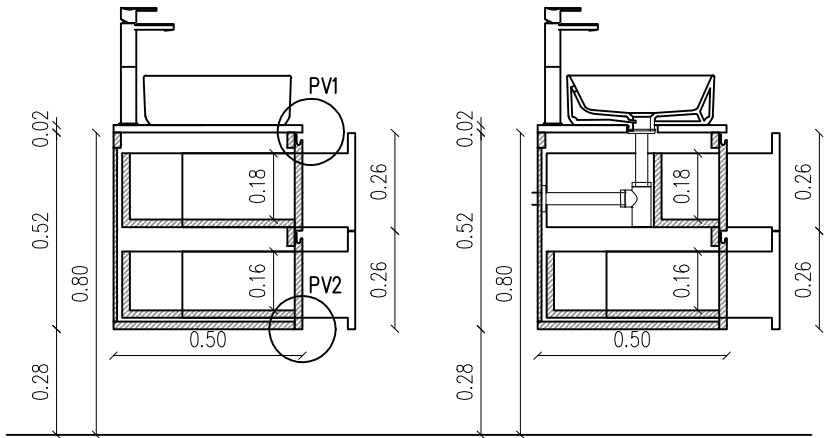


CORTE AA
ESCALA 1:20

CORTE BB
ESCALA 1:20

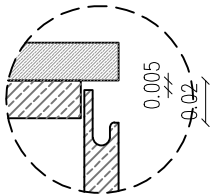

PV1
ESCALA 1:5

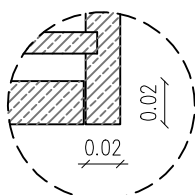

PV2
ESCALA 1:5